

ZLECENIE CIECIA

Leroy Merlin Kalisz | Dominik Maslak | dominikmaslak11@gmail.com

1. Plyta OSB-3 18 mm, arkusz 2500 x 1250 mm - KUPUJE, TNE SAM

Nie zlecam ciecicia. Plan ciecicia na stronach 2-4 - dla mnie, nie dla Państwa.

2. Plyta meblowa laminowana BIALA 18 mm - PROSZE O DOCIECIE

6 formatek 755 x 450 mm

Lacznie 2,04 m². Prosze o EXPRESS (ten sam dzien), jesli to mozliwe.

Obrzeze: prosze o oklejenie jednego dluzszego boku (755 mm) w kazdej formatce, jesli macie taka usluge. Jesli nie - kupie rolke i zrobie sam.

Czego NIE zlecam

Przegrod z arkusza OSB - ich wysokosc ustale dopiero po zamontowaniu pierwszej polki.


Starej deski z blatu biurka (moj material) - potne w domu.

Co jest dalej w tym dokumencie

- str. 2 plan ciecicia arkusza OSB (tne sam)
- str. 3 widok zabudowy regalu
- str. 4 przegrody z odpadu
- str. 5 ciecicie starej deski - w domu
- str. 6 widok zabudowy szafy - stad wymiar 755 x 450
- str. 7 lista zakupow
- str. 8 kalkulacja kosztow ciecicia

Plan ciecia - 6 polek + material na przegrody

Arkusz OSB-3 18 mm, 2500 x 1250 mm | skala 1:11 | rzaz tarczy 4 mm uwzględniony

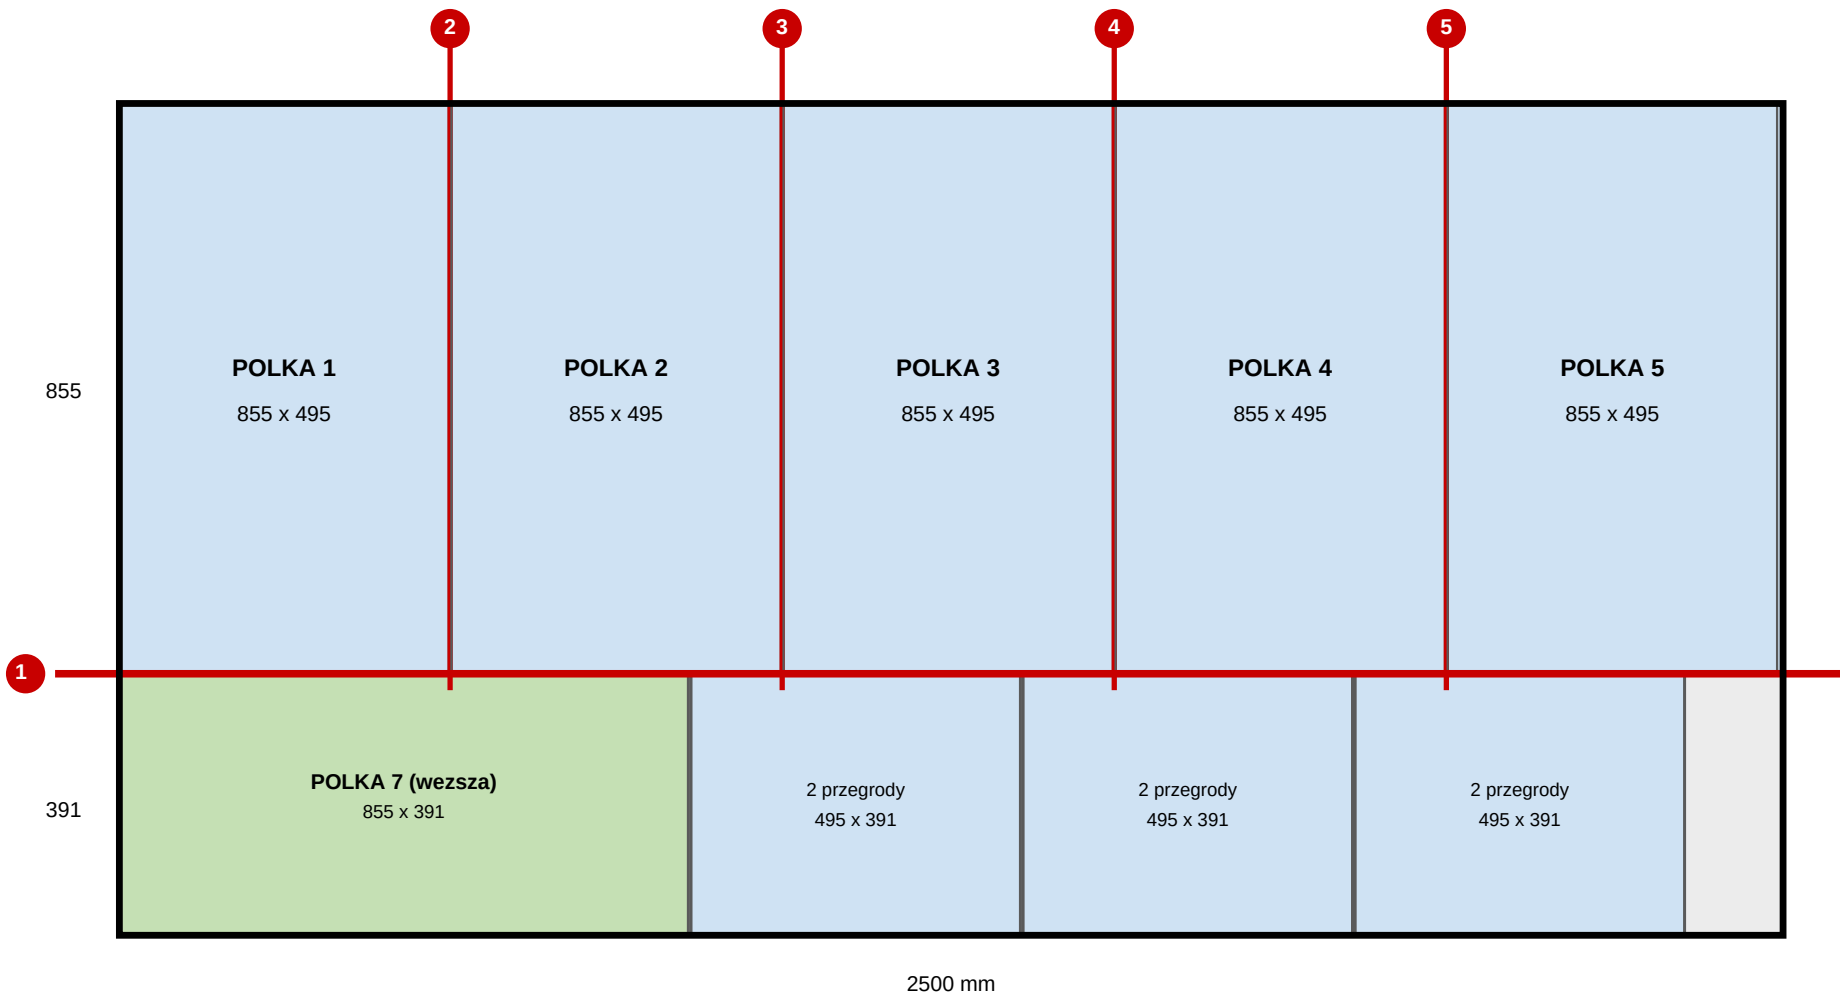

Kolejność ciec - NAJPIERW POPRZECZNE

- 1 JEDNO ciecie w poprzek calego arkusza, na 855 mm. Gorny pas idzie na 5 polek, dolny (2500 x 391) na 7. polke i przegrody.
- 2-5 cztery ciecia wzdluz pasa na polki: piec kawalkow po 495 mm (NIE po 500 - cztery rzazy zabieraja 16 mm i ostatni wyszedlby na 504 mm)
- 6-9 z dolnego pasa: 7. polka 855 x 391 (wezsza, na gora regalu),
potem 3 kawalki po 495 mm -> po dwie przegrody z kazdego.


Pierwsza polke przymierz do regalu, ZANIM potniesz reszte pasa.

Szosta polka: stara deska z blatu biurka, tnij w domu na 855 x 495 mm
(z jej odpadu 381 x 495 wychodza jeszcze 2 przegrody).

Magazyn Lozysk - warsztat/plan-ciecienia.md

Regal 2 - podział dolnej przestrzeni na 7 poziomów

widok z przodu | skala 1:11 | głębokość polek 495 mm

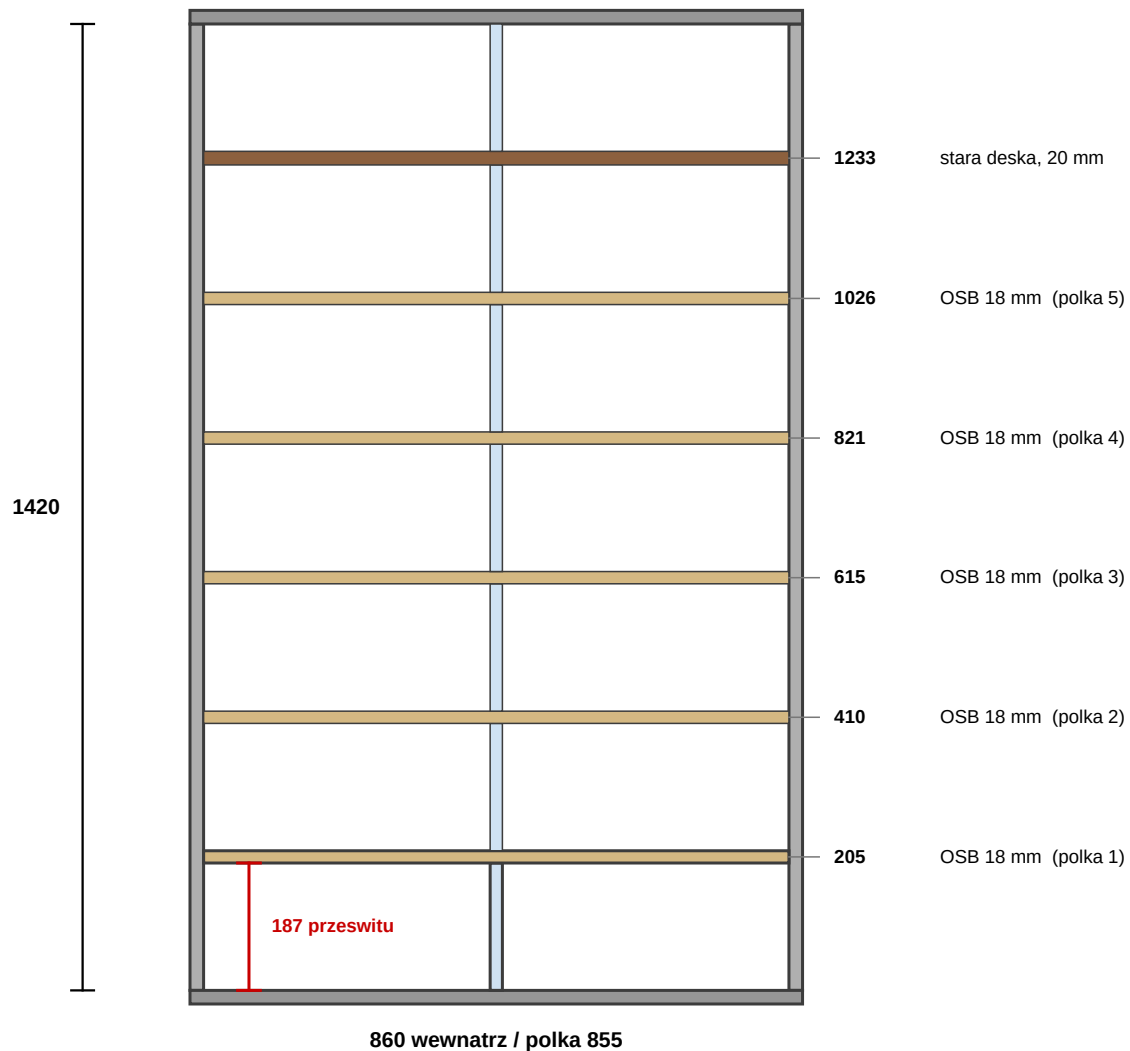

Wykaz elementów

- 5 x polka OSB-3 18 mm 855 x 495 z arkusza
- 1 x polka ze starej deski 855 x 495 blat biurka, 20 mm
- 7 x przegroda pionowa 187 x 495 z odpadu 2500 x 391
- 12 x listwa podporowa 20 x 30 x 500 do kupienia (ok. 6 m)


Po co przegroda pionowa

Dzieli rozpiętość polki z 860 na 428 mm.
Ugięcie spada z 5,7 mm do 0,35 mm - szesnastokrotnie.
Wychodzi z odpadu, więc nic nie kosztuje.
MUSZA stać jedna nad drugą - przenosić obciążenie aż na dno regalu.

Przy okazji dzieli każdą półkę na dwie części, co samo porządkuje łozyska wg rozmiaru.

Przegrody - 8 sztuk 187 x 495 mm

Każdy kawałek JEDNYM cięciem daje dwie przegrody. Potrzeba 7, wychodzi 8.

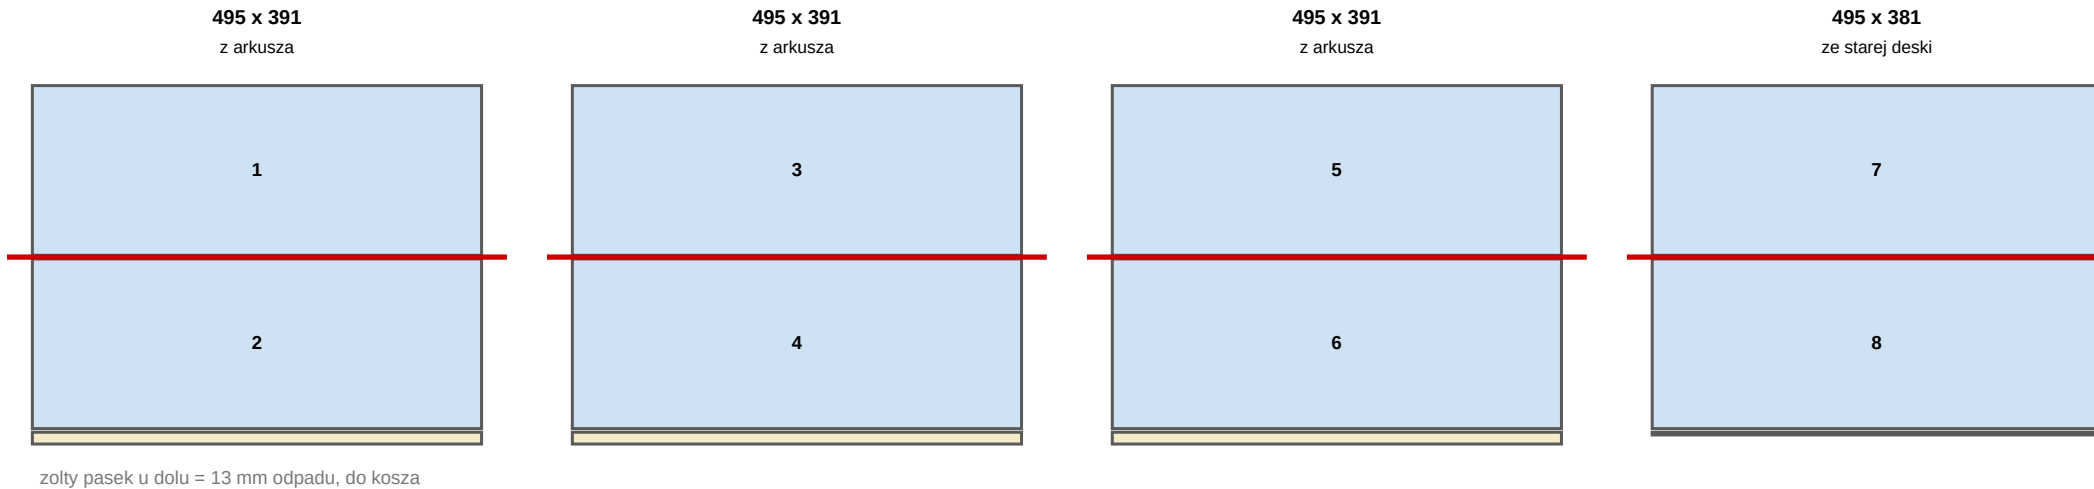

Zanim utniesz


WYSOKOSC TNIJ NA MIEJSCU, po zamontowaniu pierwszej polki. 187 mm to wyliczenie;
realne grubosci plyt roznia sie o ulamki milimetra, a bledy sumuja sie przez szesc poziomow.
Za krotka przegroda nie robi nic, za dluga podnosi polke nad podpory boczne.

Przegroda pracuje na SCISKANIE - wkrety maja ja tylko trzymac przed przewroceniem.
Dwa wkrety 3,5 x 30 od gory wystarcza, ale NAWIERC otwor 2,5 mm: wkret wbity na sile
w kant plyty rozwarstwa ja wzdluz i przegroda traci sztywnosc, czyli to, po co tam jest.

Wszystkie przegrody MUSZA stac w jednej pionowej linii - obciazenie schodzi przez nie
az na dno regalu. Odmierz srodek (430 mm od scianki) i zaznaczaj poziomica, nie na oko.

Stara deska z blatu biurka - 1 polka + 2 przegrody

1240 x 520 x 20 mm | 3 ciecia | wykorzystanie 94%

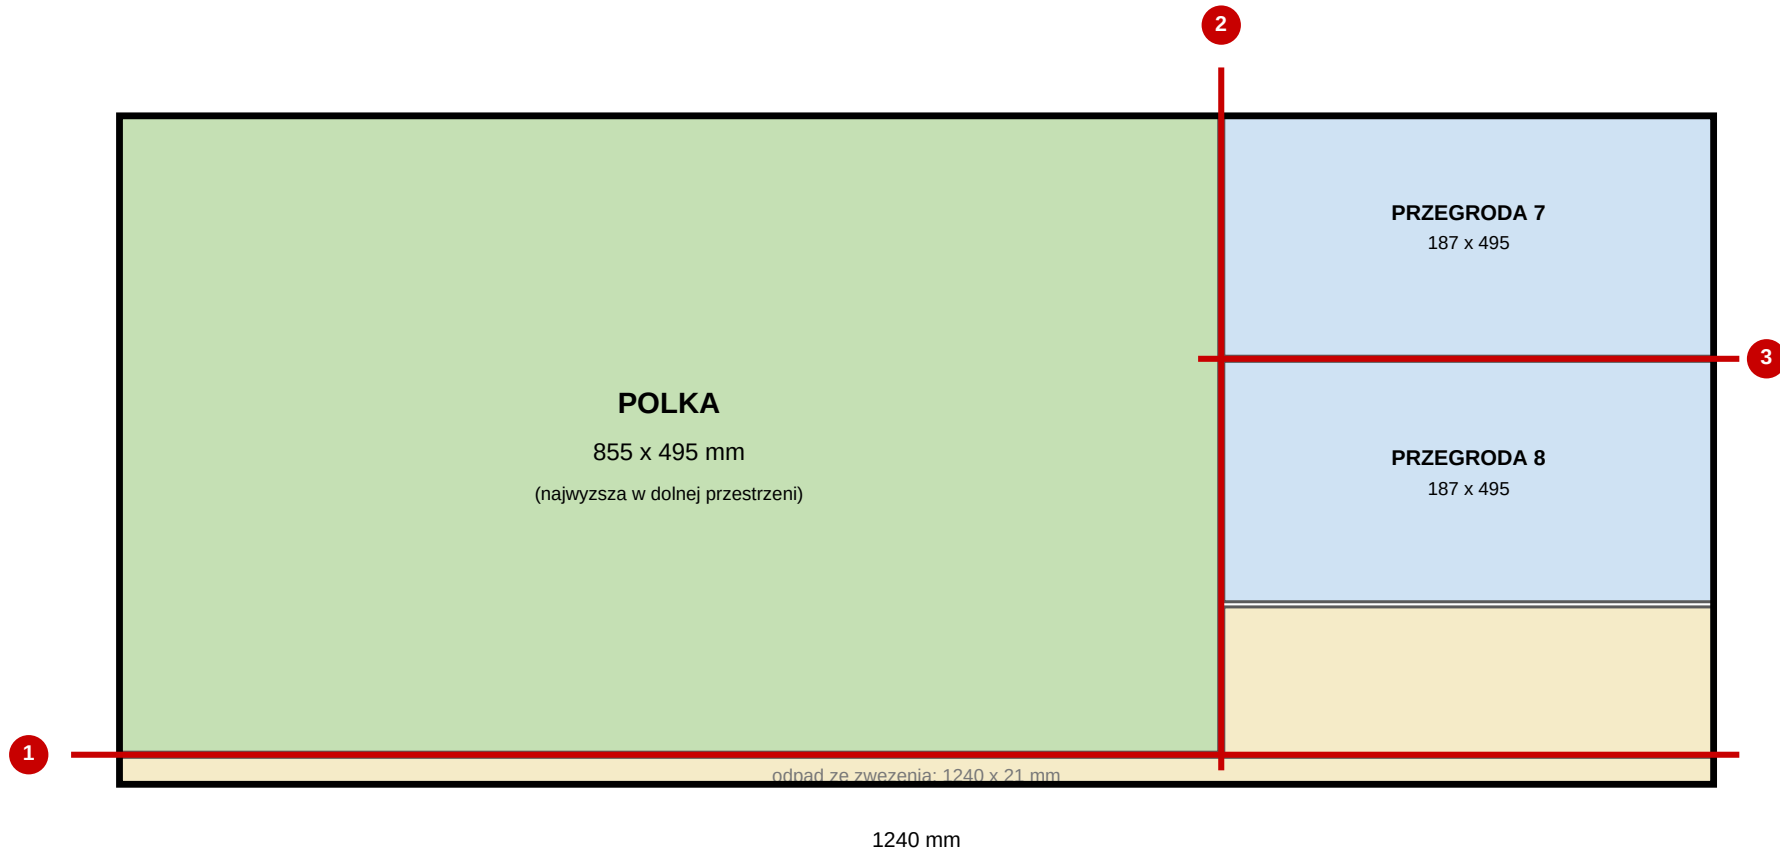

Kolejność

- 1 wzdłuż całej deski: zwężenie 520 -> 495 mm (odpada pasek 1240 x 21 mm)
- 2 w poprzek na 855 mm -> POLKA 855 x 495, zostaje kawałek 381 x 495
- 3 ten kawałek na poł -> DWIE PRZEGRODY 187 x 495 ($2 \times 187 + \text{rzaz} = 378 \leq 381$, zapas 3 mm)

Deska ma 20 mm, reszta pól 18 - to nie przeszkadza, rozstaw jest przeliczony.


Blat biurka to laminowana płyta wiorowa: **ZABEZPIECZ KRAWĘDZIE** po cieciu

(obrzeże, silikon albo farba) - laminat chroni tylko płaszczyzny, odsłonięty kąt pecznieje.

Ta deska daje polkę **NAJWYŻSZA W DOLNEJ PRZESTRZENI** (spód na 1233 mm nad dnem).

Szafy na ubrania - 3 polki w kazdej z dwoch

Przestrzen 1200 x 760 x 470 mm, scianka 16 mm | 4 poziomy po 286 mm

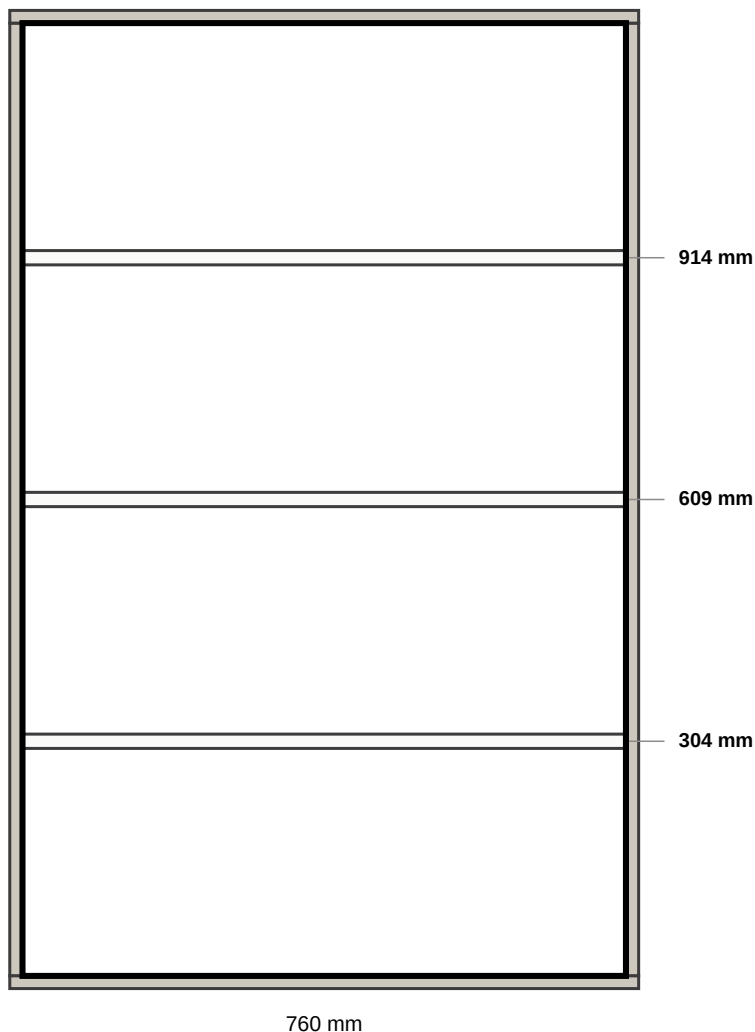

Formatki do zamowienia (na wymiar)

6 x 755 x 450 mm

plyta meblowa laminowana BIALA 18 mm

755 = 760 minus 5 mm luzu

450 zamiast 470 - 2 cm zapasu na zawiasy

razem 2.04 m²

Dlaczego 18 mm, a nie 16 jak scianki

Rozpietosc 76 cm. Ugiecie po latach, granica 3,8 mm:

16 mm: 15 kg -> 3,8 mm 20 kg -> 5,1 mm za duzo

18 mm: 15 kg -> 2,7 mm 20 kg -> 3,6 mm OK

POSCIELI I KOCOW (25-30 kg) na te polki nie kladz -
wygna kazda plyte na tej rozpietosci.

Cieta krawedz bialej plyty to gola wiorowa - oklej
obrzezem przednie krawedzie, razem 4,5 m.

LISTA ZAKUPOW - jeden wyjazd, dwa projekty

ulozona dzialami sklepu

DZIAL PLYT

OSB-3 18 mm, arkusz 250 x 125 cm (kod 43226043)	1 szt.	104 zł
plyta laminowana BIALA 18 mm - DOCIETA NA WYMIAR	2,04 m2	~78 zł
zamowienie: 6 formatek 755 x 450 mm		

DZIAL DREWNA

listwa montazowa sosnowa 20 x 30 x 2700 (kod 45216185)	4 szt.	~48 zł
--	--------	--------

DZIAL METALOWY

wkrety do drewna 4 x 35 mm, OCYNKOWANE	100 szt.	~25 zł
wkrety do drewna 3,5 x 30 mm, OCYNKOWANE	100 szt.	~20 zł
podporki do polek, kolek 5 mm	24 szt.	~15 zł

DZIAL WYKONCZENIA

obrzeze melaminowe biale 18-19 mm, rolka 5 m	1-2 szt.	~30 zł
--	----------	--------

RAZEM

~320 zł

(regal na lozyska ~197 zł + szafy ~123 zł, plus oplata za dociecie)

NA CO UWAZAC

Wkretow NIE zaokraglaj w gore: scianka regalu ma 20 mm, scianka szafy 16 -
wkret 40 mm przebijie jedna i druga na wylot.
Nie bierz wkretow nierdzewnych, sa kilka razy drozsze i do wnetrza niepotrzebne.
Nie bierz calego arkusza bialej plyty: 220 zł za 5,8 m2, gdy potrzebujesz 2 m2.
Zapytaj PRZEZ TELEFON o cene dociecia - zalezy od sklepu i potrafi zaskoczyc.

KOSZT CIECIA - cztery scenariusze

Leroy Merlin Kalisz: ciecie proste 3 zl (termin 2-3 dni), EXPRESS tego samego dnia 6 zl

Ile ciec i gdzie

Arkusz OSB-3 (5 polek + 7. polka + 3 kawalki na przegrody)

9 LEROY

Plyta biala - 6 formatek 755 x 450

6 LEROY

Podzial kawalkow na przegrody 187 x 495

4 W DOMU

Stara deska z blatu biurka

3 W DOMU

Przegrod NIE zlecaj w Leroy. Wysokosc 187 mm to wyliczenie - realna wychodzi z pomiaru po zamontowaniu pierwszej polki. Ciecie w ciemno kosztowaloby 12 zl i moglo sie nie zgadzac.

Starej deski Leroy nie potnie - to nie ich material.

Scenariusz	Ciec	Za ciecie	Termin	RAZEM
A. Wszystko tnie Leroy, termin standardowy	15	45 zl	2-3 dni	365 zl
B. OSB tnie sam w kaciku, biala w Leroy	6	18 zl	2-3 dni	338 zl
C. Wszystko tnie Leroy, EXPRESS	15	90 zl	ten sam dzien	410 zl
D. OSB tnie sam, biala EXPRESS	6	36 zl	ten sam dzien	356 zl

Rekomendacja: scenariusz D

Biala plyta MUSI byc ciecia w sklepie - jest widoczna w szafie, a ciecie reczna pilarka zostawia poszarpana krawedz, ktorej obrzeze nie zakryje. 6 ciec, 36 zl za express, i wyjezdzasz z gotowymi formatkami tego samego dnia.

OSB tniesz sam: to warsztat, krawedzi nie widac, a 27 zl za dziewiec ciec przy 104-zlotowym arkuszu to ponad jedna czwarta ceny plyty.

Roznica A kontra D: 9 zl. Roznica B kontra D: 18 zl za to, ze nie wracasz po trzech dniach po odbior.