


Plan ciecia - 6 polek + material na przegrody

Arkusz OSB-3 18 mm, 2500 x 1250 mm | skala 1:11 | rzaz tarczy 4 mm uwzględniony

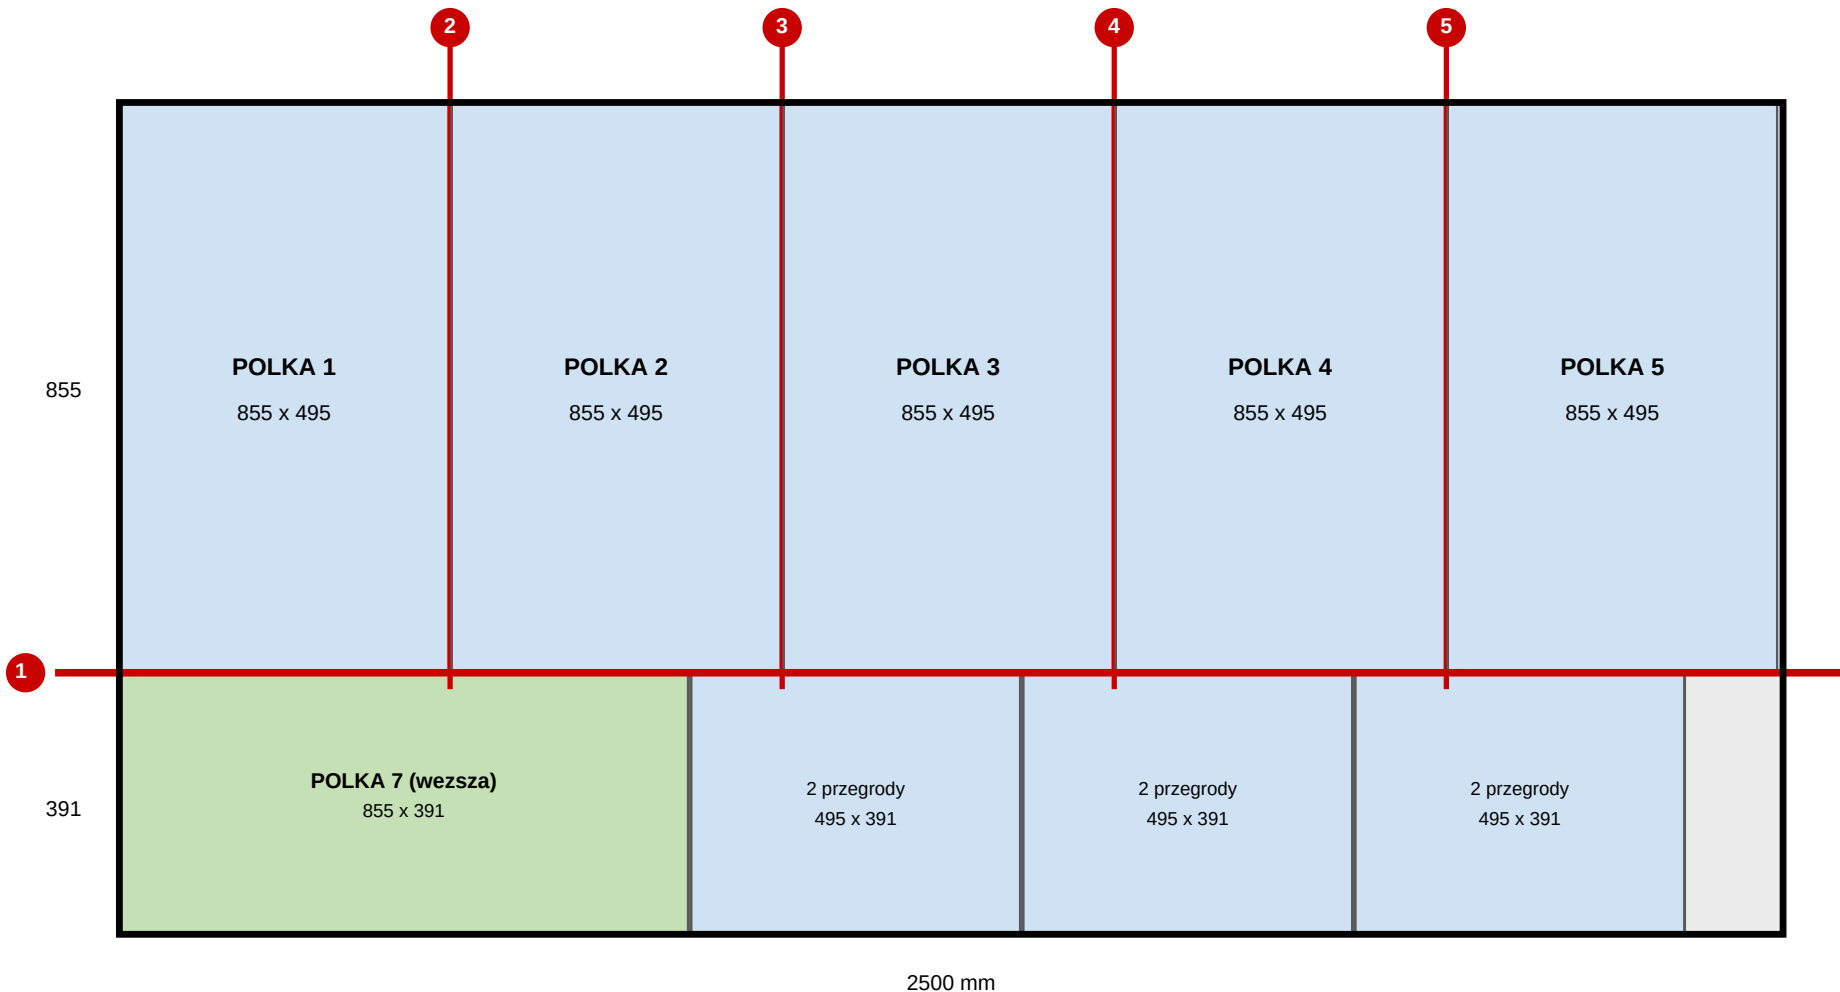

Kolejność ciec - NAJPIERW POPRZECZNE

- 1 JEDNO ciecie w poprzek calego arkusza, na 855 mm. Gorny pas idzie na 5 polek, dolny (2500 x 391) na 7. polke i przegrody.
- 2-5 cztery ciecia wzdluz pasa na polki: piec kawalkow po 495 mm (NIE po 500 - cztery rzazy zabieraja 16 mm i ostatni wyszedlby na 504 mm)
- 6-9 z dolnego pasa: 7. polka 855 x 391 (wezsza, na gora regalu),
potem 3 kawalki po 495 mm -> po dwie przegrody z kazdego.


Pierwsza polke przymierz do regalu, ZANIM potniesz reszte pasa.

Szosta polka: stara deska z blatu biurka, tnij w domu na 855 x 495 mm
(z jej odpadu 381 x 495 wychodza jeszcze 2 przegrody).

Projekt wygenerowany automatycznie - Magazyn Lozysk

Regal 2 - podział dolnej przestrzeni na 7 poziomów

widok z przodu | skala 1:11 | głębokość polek 495 mm

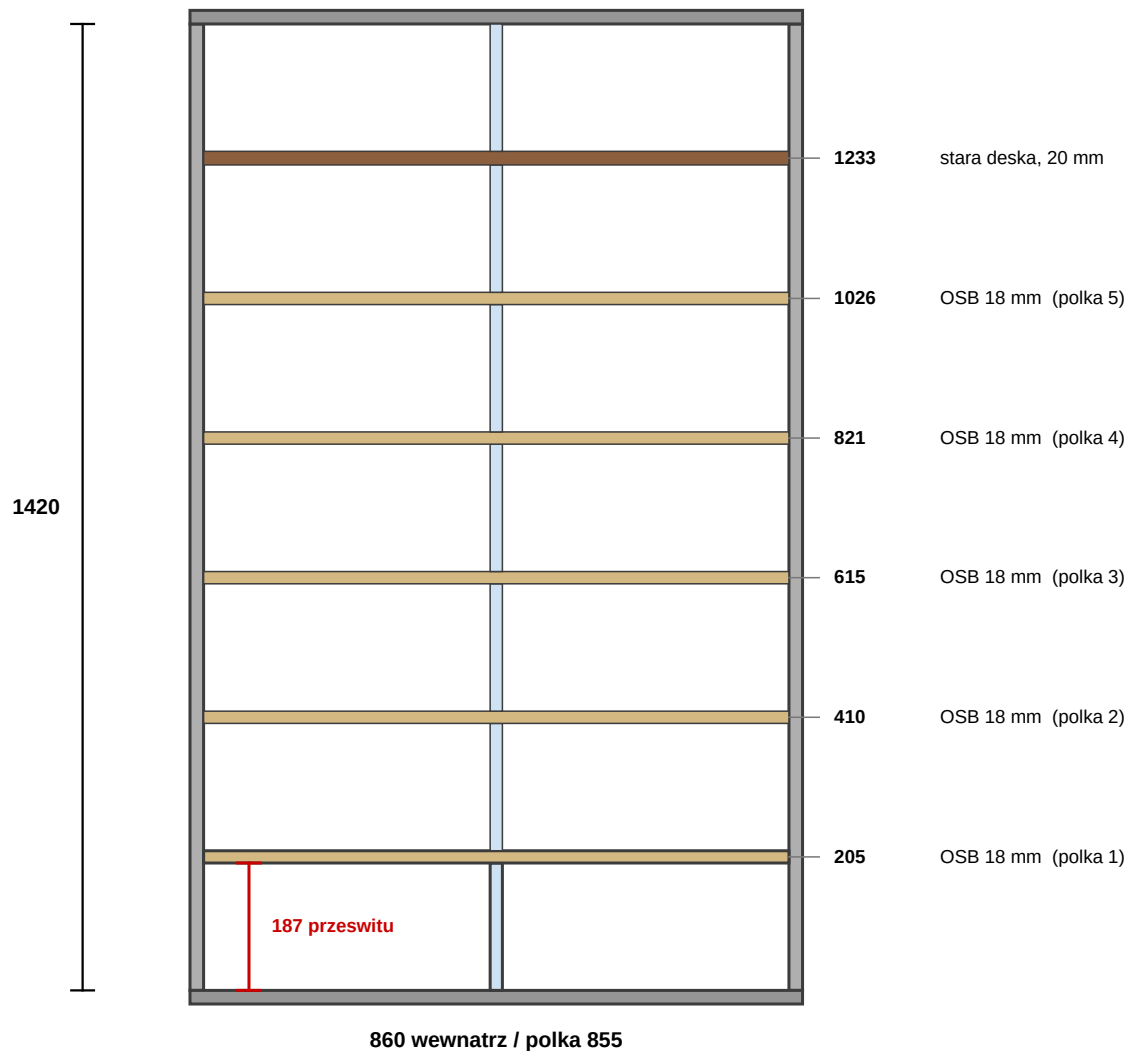

Wykaz elementów

- 5 x polka OSB-3 18 mm 855 x 495 z arkusza
- 1 x polka ze starej deski 855 x 495 blat biurka, 20 mm
- 7 x przegroda pionowa 187 x 495 z odpadu 2500 x 391
- 12 x listwa podporowa 20 x 30 x 500 do kupienia (ok. 6 m)


Po co przegroda pionowa

Dzieli rozpiętość polki z 860 na 428 mm.
Ugięcie spada z 5,7 mm do 0,35 mm - szesnastokrotnie.
Wychodzi z odpadu, więc nic nie kosztuje.
MUSZA stać jedna nad drugą - przenosić obciążenie aż na dno regału.

Przy okazji dzieli każdą półkę na dwie części,
co samo porządkuje łozyska wg rozmiaru.

Przegrody - 8 sztuk 187 x 495 mm

Każdy kawałek JEDNYM cięciem daje dwie przegrody. Potrzeba 7, wychodzi 8.

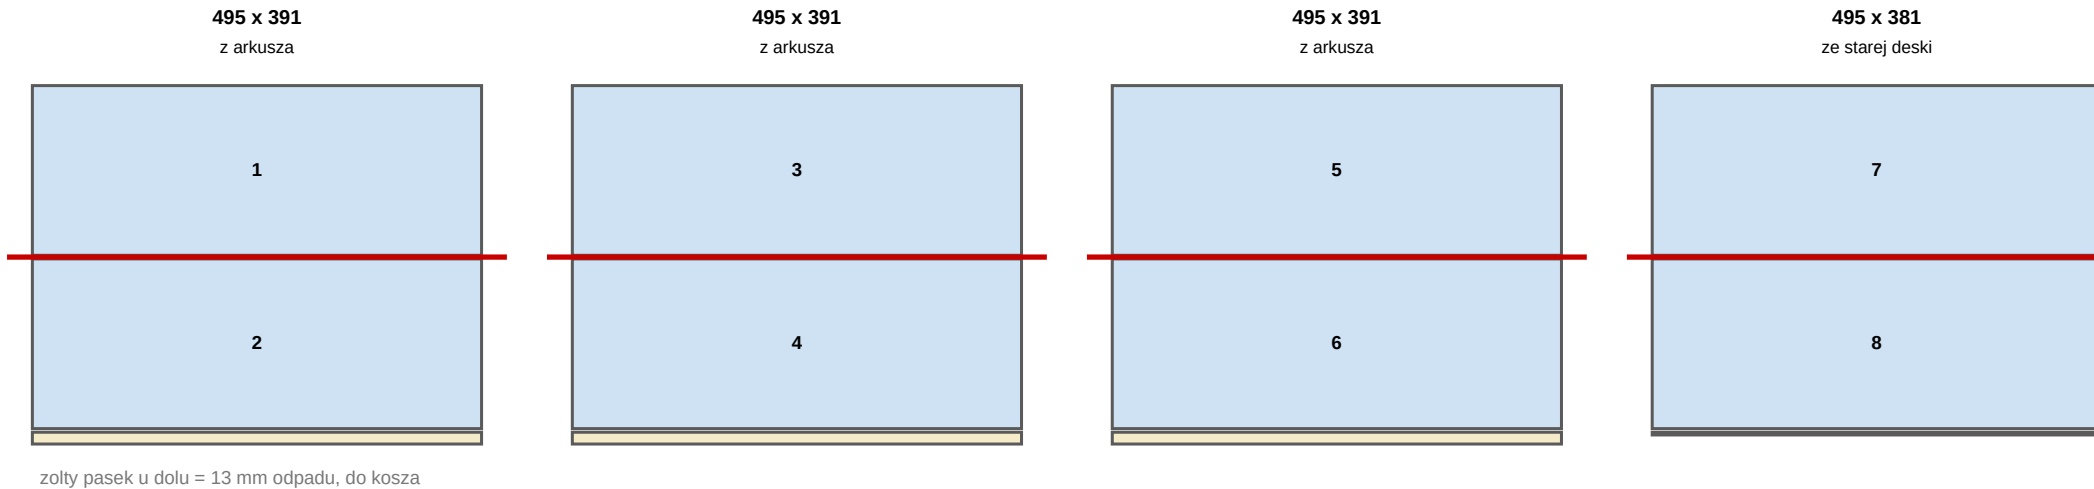

Zanim utniesz


WYSOKOSC TNIJ NA MIEJSCU, po zamontowaniu pierwszej polki. 187 mm to wyliczenie;
realne grubosci plyt roznia sie o ulamki milimetra, a bledy sumuja sie przez szesc poziomow.
Za krotka przegroda nie robi nic, za dluga podnosi polke nad podpory boczne.

Przegroda pracuje na SCISKANIE - wkrety maja ja tylko trzymac przed przewroceniem.
Dwa wkrety 3,5 x 30 od gory wystarcza, ale NAWIERC otwor 2,5 mm: wkret wbity na sile
w kant plyty rozwarstwa ja wzdluz i przegroda traci sztywnosc, czyli to, po co tam jest.

Wszystkie przegrody MUSZA stac w jednej pionowej linii - obciazenie schodzi przez nie
az na dno regalu. Odmierz srodek (430 mm od scianki) i zaznaczaj poziomica, nie na oko.

Stara deska z blatu biurka - 1 polka + 2 przegrody

1240 x 520 x 20 mm | 3 ciecia | wykorzystanie 94%

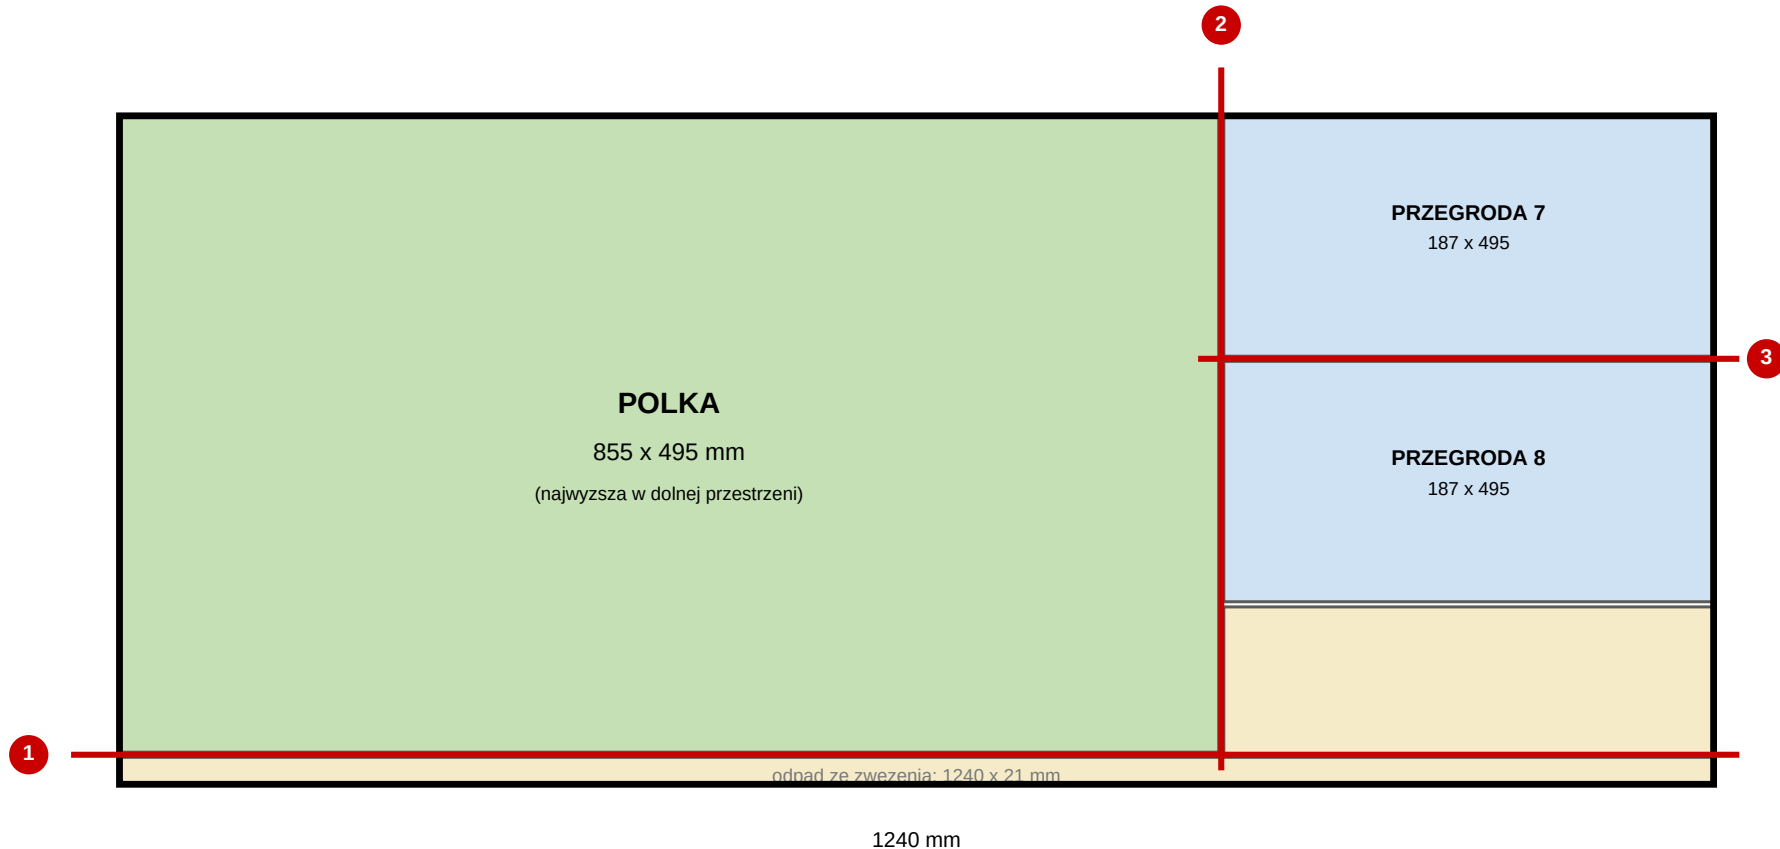

Kolejność

- 1 wzdłuż całej deski: zwężenie 520 -> 495 mm (odpada pasek 1240 x 21 mm)
- 2 w poprzek na 855 mm -> POLKA 855 x 495, zostaje kawałek 381 x 495
- 3 ten kawałek na pol -> DWIE PRZEGRODY 187 x 495 ($2 \times 187 + \text{rzaz} = 378 \leq 381$, zapas 3 mm)

Deska ma 20 mm, reszta pól 18 - to nie przeszkadza, rozstaw jest przeliczony.


Błat biurka to laminowana płyta wiorowa: **ZABEZPIECZ KRAWĘDZIE** po cieciu

(obrzeże, silikon albo farba) - laminat chroni tylko płaszczyzny, odsłonięty kąt pecznieje.

Ta deska daje polkę **NAJWYŻSZA W DOLNEJ PRZESTRZENI** (spód na 1233 mm nad dnem).

Szafy na ubrania - 3 polki w kazdej z dwoch

Przestrzen 1200 x 760 x 470 mm, scianka 16 mm | 4 poziomy po 286 mm

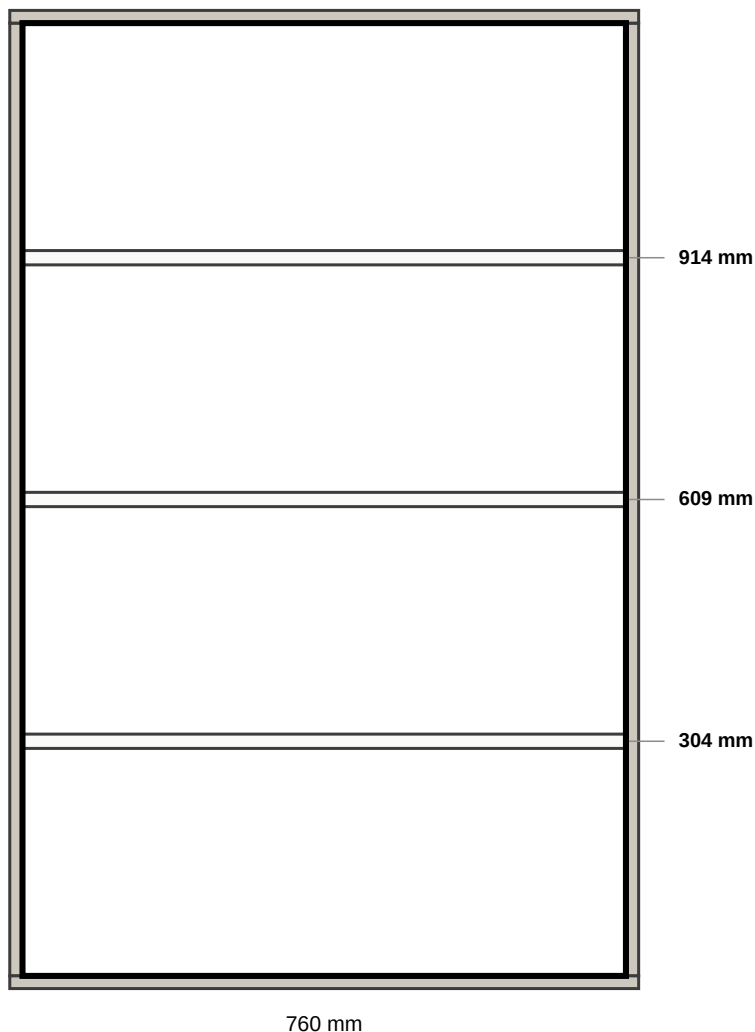

Formatki do zamowienia (na wymiar)

6 x 755 x 450 mm

plyta meblowa laminowana BIALA 18 mm

755 = 760 minus 5 mm luzu

450 zamiast 470 - 2 cm zapasu na zawiasy
razem 2.04 m²

Dlaczego 18 mm, a nie 16 jak scianki

Rozpietosc 76 cm. Ugiecie po latach, granica 3,8 mm:

16 mm: 15 kg -> 3,8 mm 20 kg -> 5,1 mm za duzo

18 mm: 15 kg -> 2,7 mm 20 kg -> 3,6 mm OK

POSCIELI I KOCOW (25-30 kg) na te polki nie kladz -
wygna kazda plyte na tej rozpietosci.

Cieta krawedz bialej plyty to gola wiorowa - oklej
obrzezem przednie krawedzie, razem 4,5 m.

ZAPOTRZEBOWANIE MATERIALOWE

dwa projekty - regal warsztatowy i polki do dwóch szaf

Pozycja	Ilosc	Macie?	Cena j.	Termin
Płyta OSB-3 18 mm, arkusz 2500 x 1250 mm	1 szt.			
Płyta wiorowa laminowana BIALA 18 mm, dociecie na wymiar	2,04 m2			
-> 6 formatek 755 x 450 mm, obrzeze na 1 dluzszym boku				
Listwa sosnowa 20 x 30 mm, dl. 2,7 m (lub kantowka 20x30)	4 szt.			
Wkrety do drewna 4 x 35 mm, ocynkowane	100 szt.			
Wkrety do drewna 3,5 x 30 mm, ocynkowane	100 szt.			
Podporki do polek, kolek 5 mm, metalowe	24 szt.			
Obrzeze melaminowe biale 18-19 mm z klejem, rolka 5 m	2 szt.			
USLUGA: ciecie plyty na wymiar	9 ciec			
Uzyteczne odpady po docinaniu, od ok. 40 x 40 cm	wg dostepnosci			

Uwagi do zamowienia

Wkrety NIE dluzsze niz podane: scianka regalu ma 20 mm, scianka szafy 16 mm.
Dluzszy wkret przebijie ja na wylot.

Płyta biała jest widoczna w otwartej szafie - ciete krawedzie wymagaja obrzeza.
Jesli oklejacie w ramach uslugi, prosze o wycene zamiast rolki.

Jesli czesc pozycji odpada, prosze o wycene reszty - i tak wole kupic na miejscu.

Rysunki na poprzednich stronach pokazuja, do czego te materialy sluza:
plan ciecia arkusza, widok zabudowy regalu i widok zabudowy szafy.